


INPUT — what you are given

Architect's FIRST FLOOR PLAN

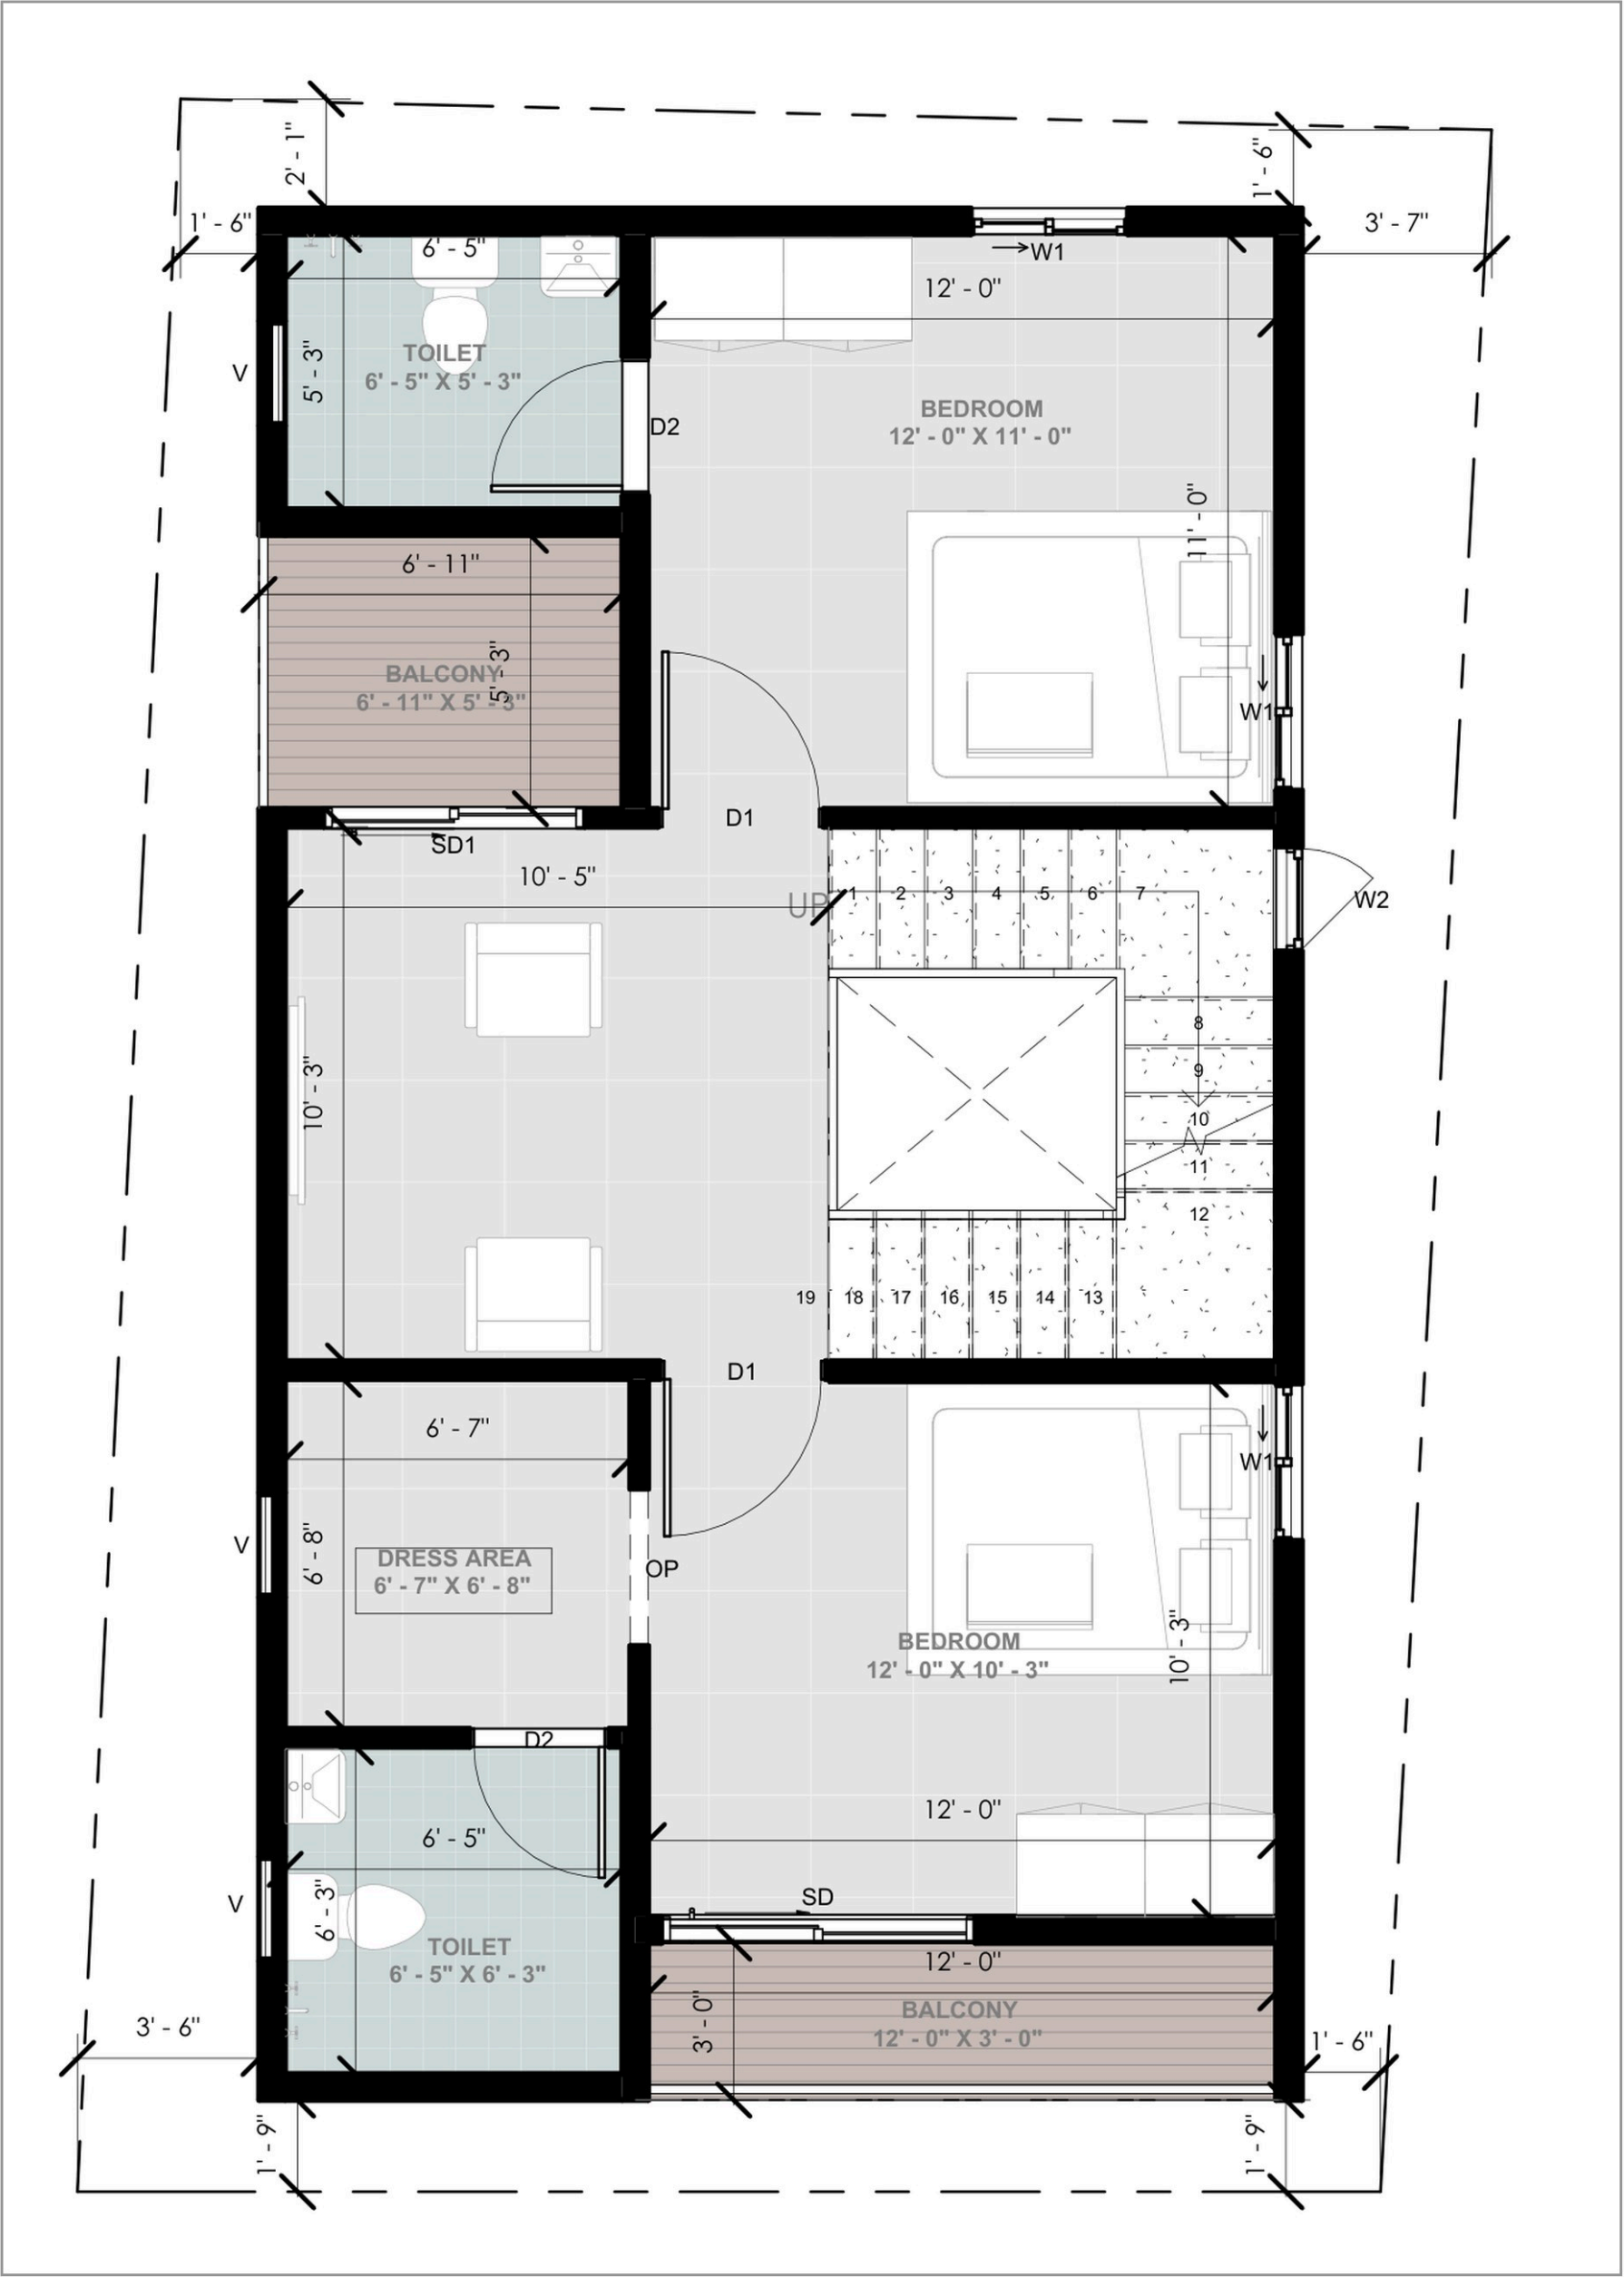

CRN574114 (Mrs. Parvathi) — first floor, 649 SF. Framing sheet 6 of 14, GROUND FLOOR ROOF FRAMING & SLAB DETAILS.
11 beams B1–B11 at 6"x18", grid A–D / 1–4. Note the plot is skewed: corners 91° / 88° / 87° / 93°, sides 40'-1" vs 39'-6".

TARGET — what you must work out

Structural FRAMING for the same floor

