


INPUT — what you are given

Architect's FIRST FLOOR PLAN

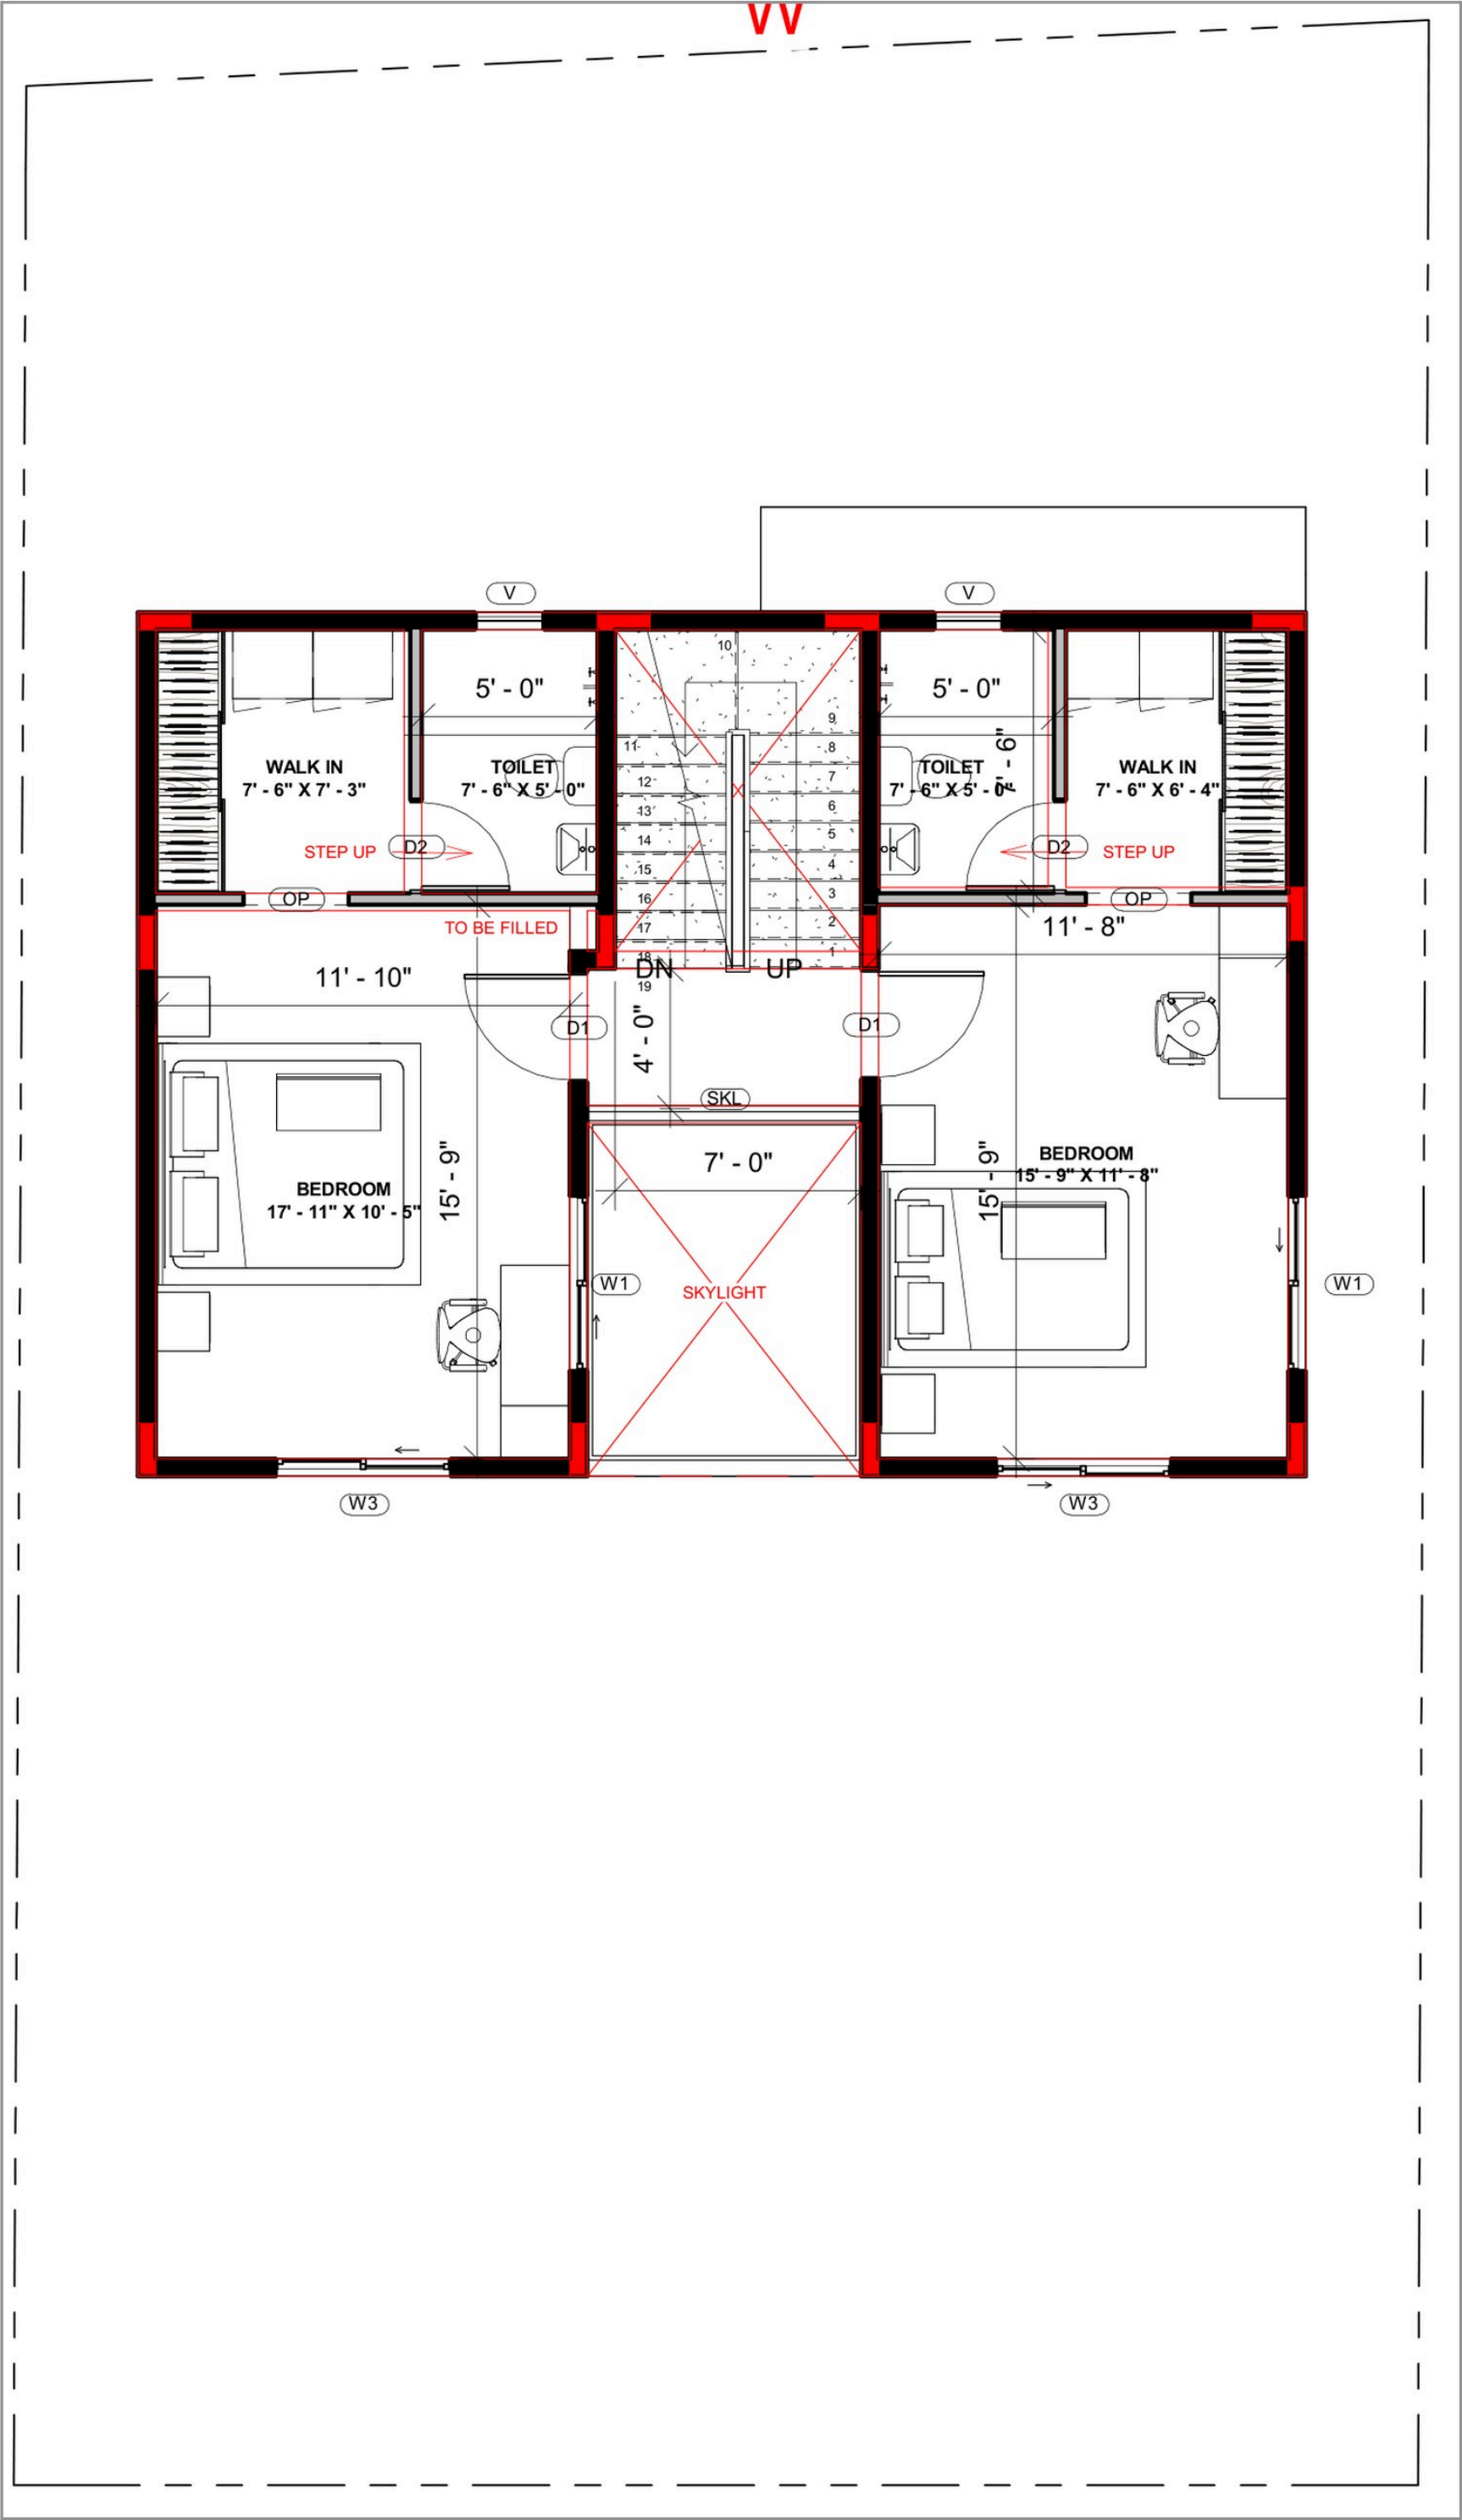

TARGET — what you must work out

Structural FRAMING for the same floor

