
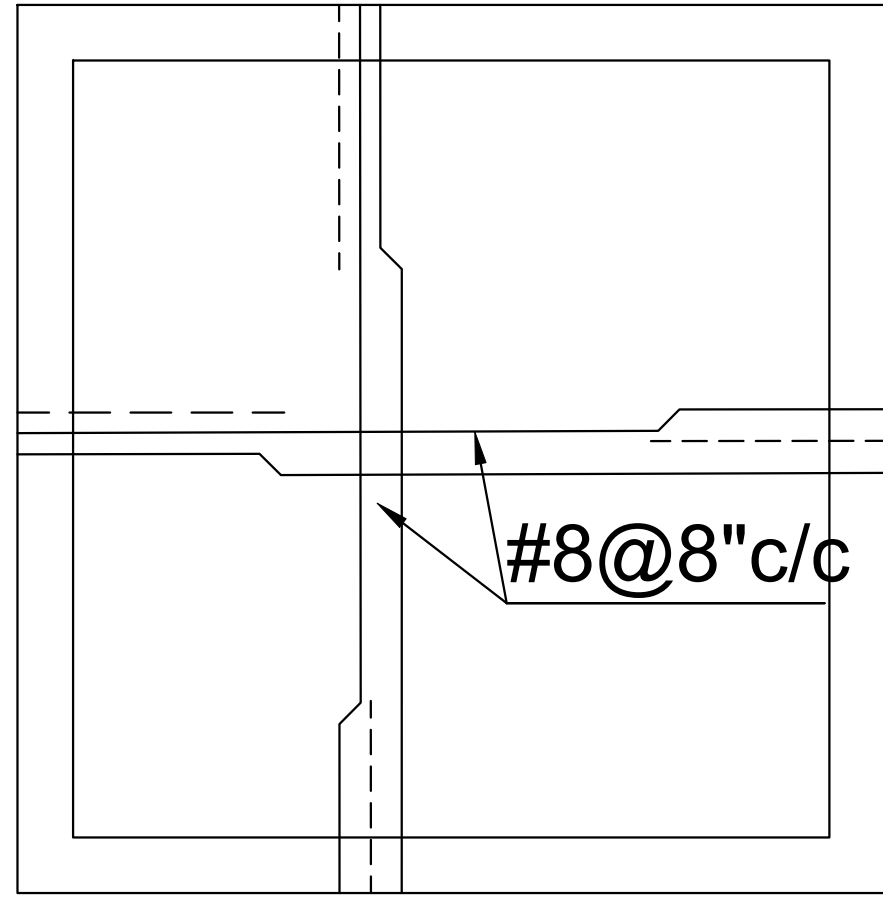


## BEAM LEGEND:

8" X 18"

## SLAB LEGEND:


6" THICK

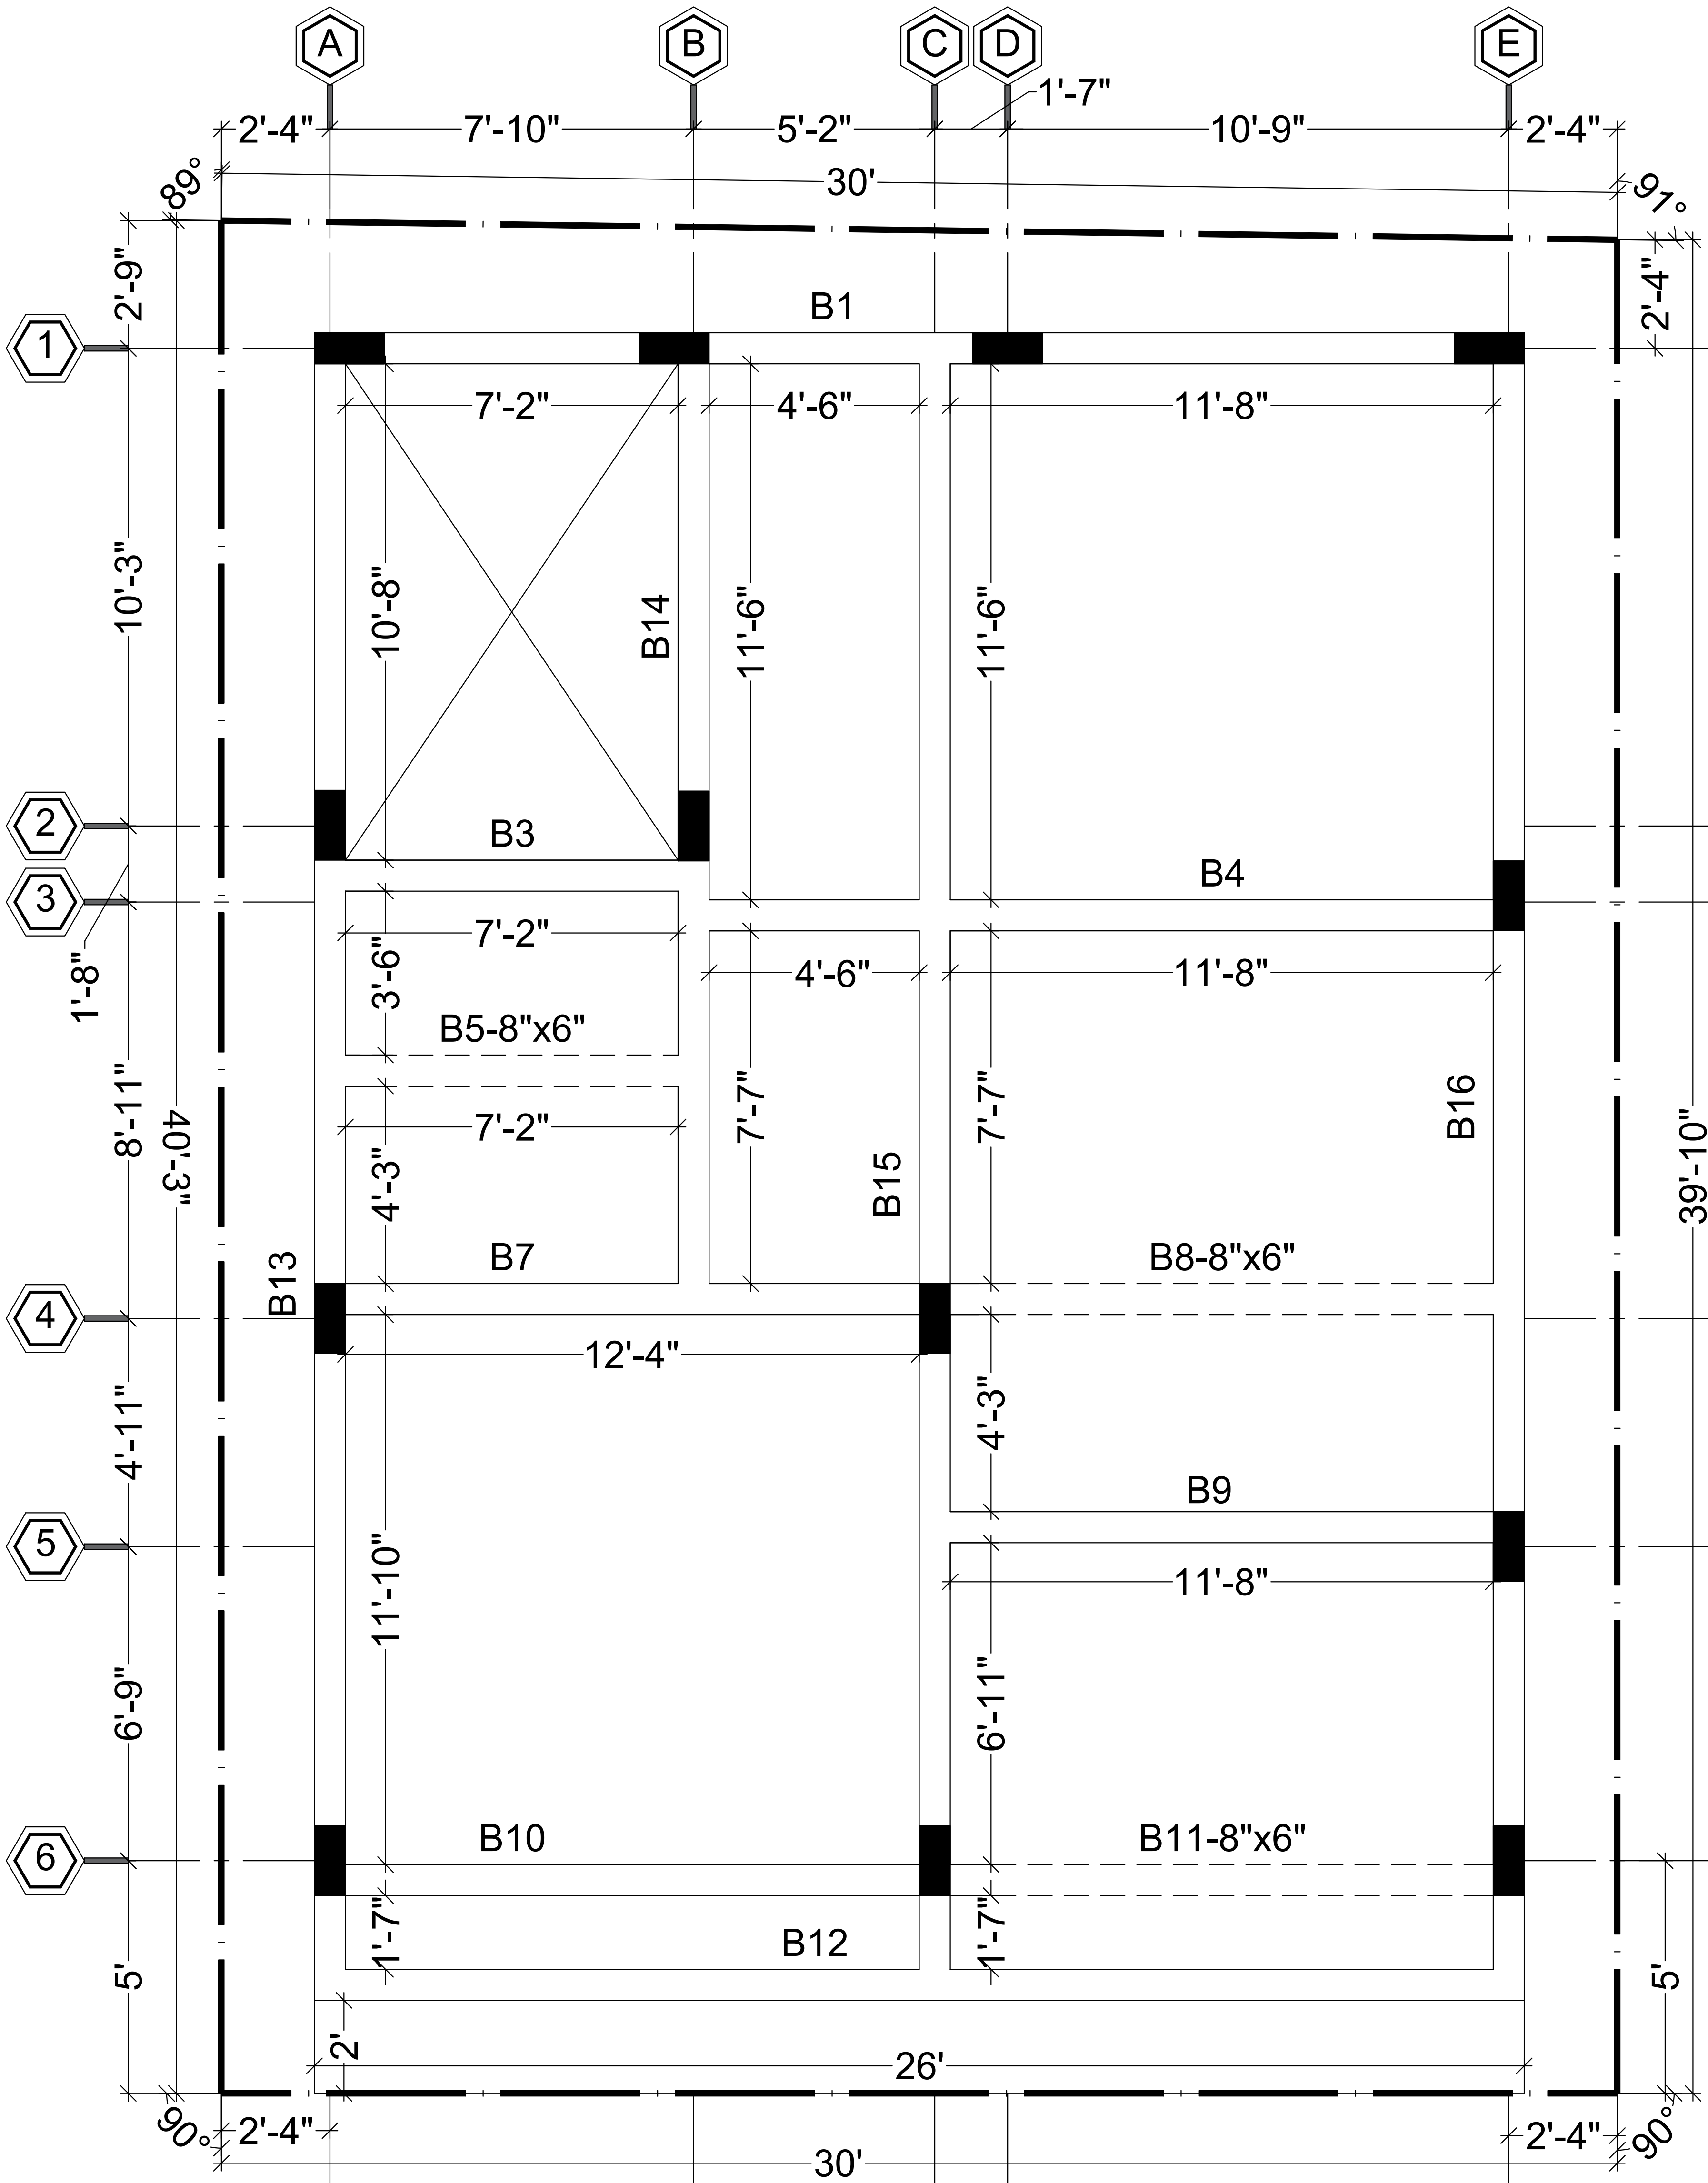

TYPICAL SLAB DETAILS

## Slab Notes:

1. SLAB THICKNESS = 6" Unless specified otherwise
2. Use M25 concrete mix for slab
3. Extrabars at continuous edj 0.3L on either side of the beam
4. Crank alternate bar at 0.25L on either side of the beam.
5. Extrabar at discontinuous edj 0.1L
6. Provide Distribution steel 8mm @8" c/c wherever require

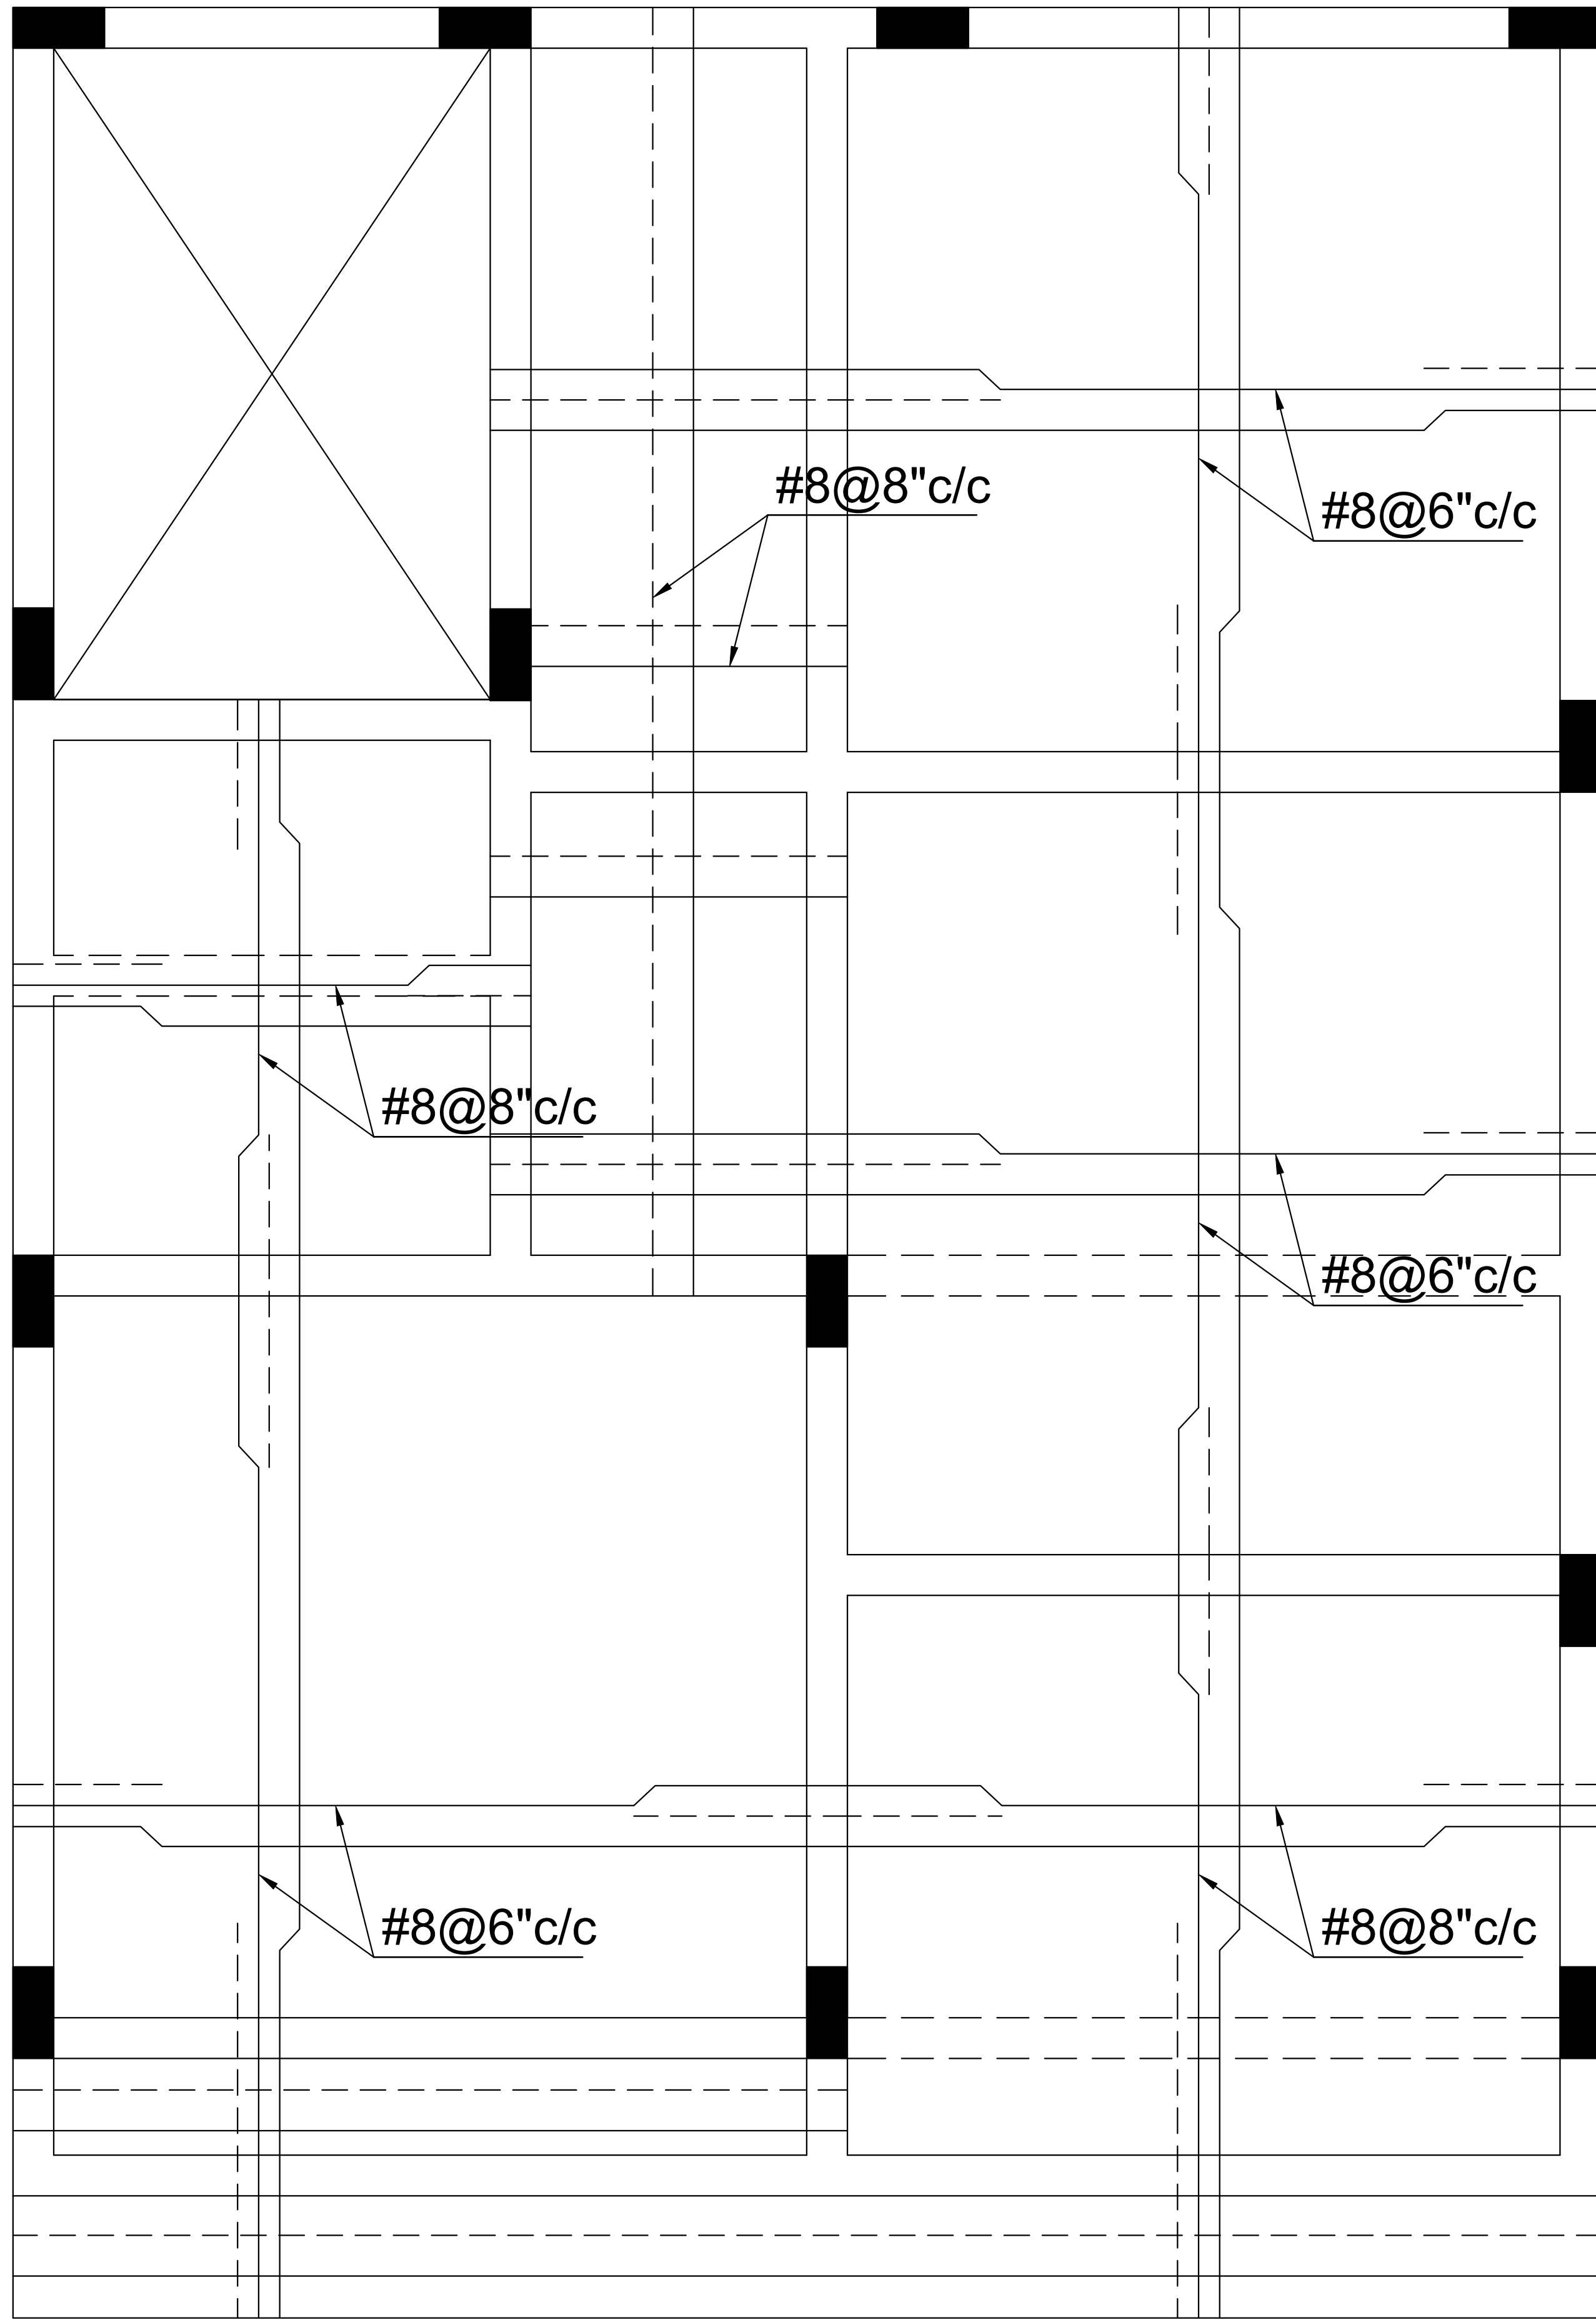

B2,B3 BEAM NUMBERS ARE NOT USED.

## IMPORTANT NOTICE:

DURING EXCAVATION, IF ANY LOOSE PACKETS OF SOIL ARE ENCOUNTERED, IT IS CRUCIAL THAT THESE ARE IMMEDIATELY BROUGHT TO THE NOTICE OF THE STRUCTURAL CONSULTANT FOR ASSESSMENT AND GUIDANCE.

RETAINING WALL / SUMP TO BE BACK FILLED ONLY AFTER THE CONSTRUCTION OF CONNECTING GRADE SLAB ,STIFFENER BEAM AND FLOOR SLABS.

## NOTES:

1. PLEASE DO NOT SCALE THIS DRAWING.FOLLOW ONLY WRITTEN DIMENSIONS.
2. THIS BUILDING IS DESIGNED FOR G+3 FLOOR.
3. THIS DRAWING TO BE READ IN CONJUNCTION WITH THE RELEVANT ARCHITECTURAL, ELECTRICAL, PLUMBING DRAWINGS.
4. LAPS SHOULD BE STAGGERED & SHOULD NOT BE MORE THAN 50% AT ANY LOCATION.
5. CLEAR COVERS FOR  
A) FOOTINGS 50 MM  
B) COLUMNS 40 MM  
C) BEAMS 25 MM  
D) R.C.C SLAB 20 MM
6. LAP LENGTHS FOR  
COLUMNS : 40 X DIA OF BARS.  
BEAMS & SLABS : 48 X DIA OF BARS.
7. LAP SHOULD BE AVOIDED IN TENSION ZONES.
8. SBC OF THE SOIL IS TAKEN AS 250 Kn/m<sup>2</sup> AT 1.5 m FROM THE NATURAL OR UP TO HARD STRATA WHICHEVER IS MAX.
9. THE BUILDING IS DESIGNED AS PER RELEVANT I.S CODES.
- 10.GRADE OF CONCRETE IS M25.
- 11.GRADE OF STEEL IS Fe550.
12. ALL DIMENSIONS ARE IN FEET & INCHES
- 13.REFER ARCHI. DRAWING FOR ALL LEVELS,DUCTS & DIMENSIONS.

| Rev. No | Revision | Date |
|---------|----------|------|
|         |          |      |
|         |          |      |
|         |          |      |

PROJECT ID :

CRN716485

PROJECT NAME:

PROPOSED RESIDENCE FOR Mr.SACHIN

STRUCTURAL CONSULTANTS:



Mobile: +91-9844490190

Address :

#41, Nobel Residency Road,  
Doddakammanahalli,  
Bangalore-560076

Email: rk.designengineers@gmail.com

Website: www.rkdesignengineers.com

ARCHITECTS:

**Brick & Bolt**  
HOME & COMMERCIAL CONSTRUCTION

DRAWING TITLE:

GROUND FLOOR ROOF FRAMING & SLAB  
DETAILS

|                |                       |          |            |                                                                                                |   |
|----------------|-----------------------|----------|------------|------------------------------------------------------------------------------------------------|---|
| Drawn By       | KR                    | Scale    | N.T.S      | Rev.                                                                                           | R |
| Design By      | SKR                   | Date     | 26-01-2026 | <br>NORTH |   |
| Checked By     | RK                    | Sheet No | 6 OF 14    |                                                                                                |   |
| DRAWING STATUS | GOOD FOR CONSTRUCTION |          |            |                                                                                                |   |