


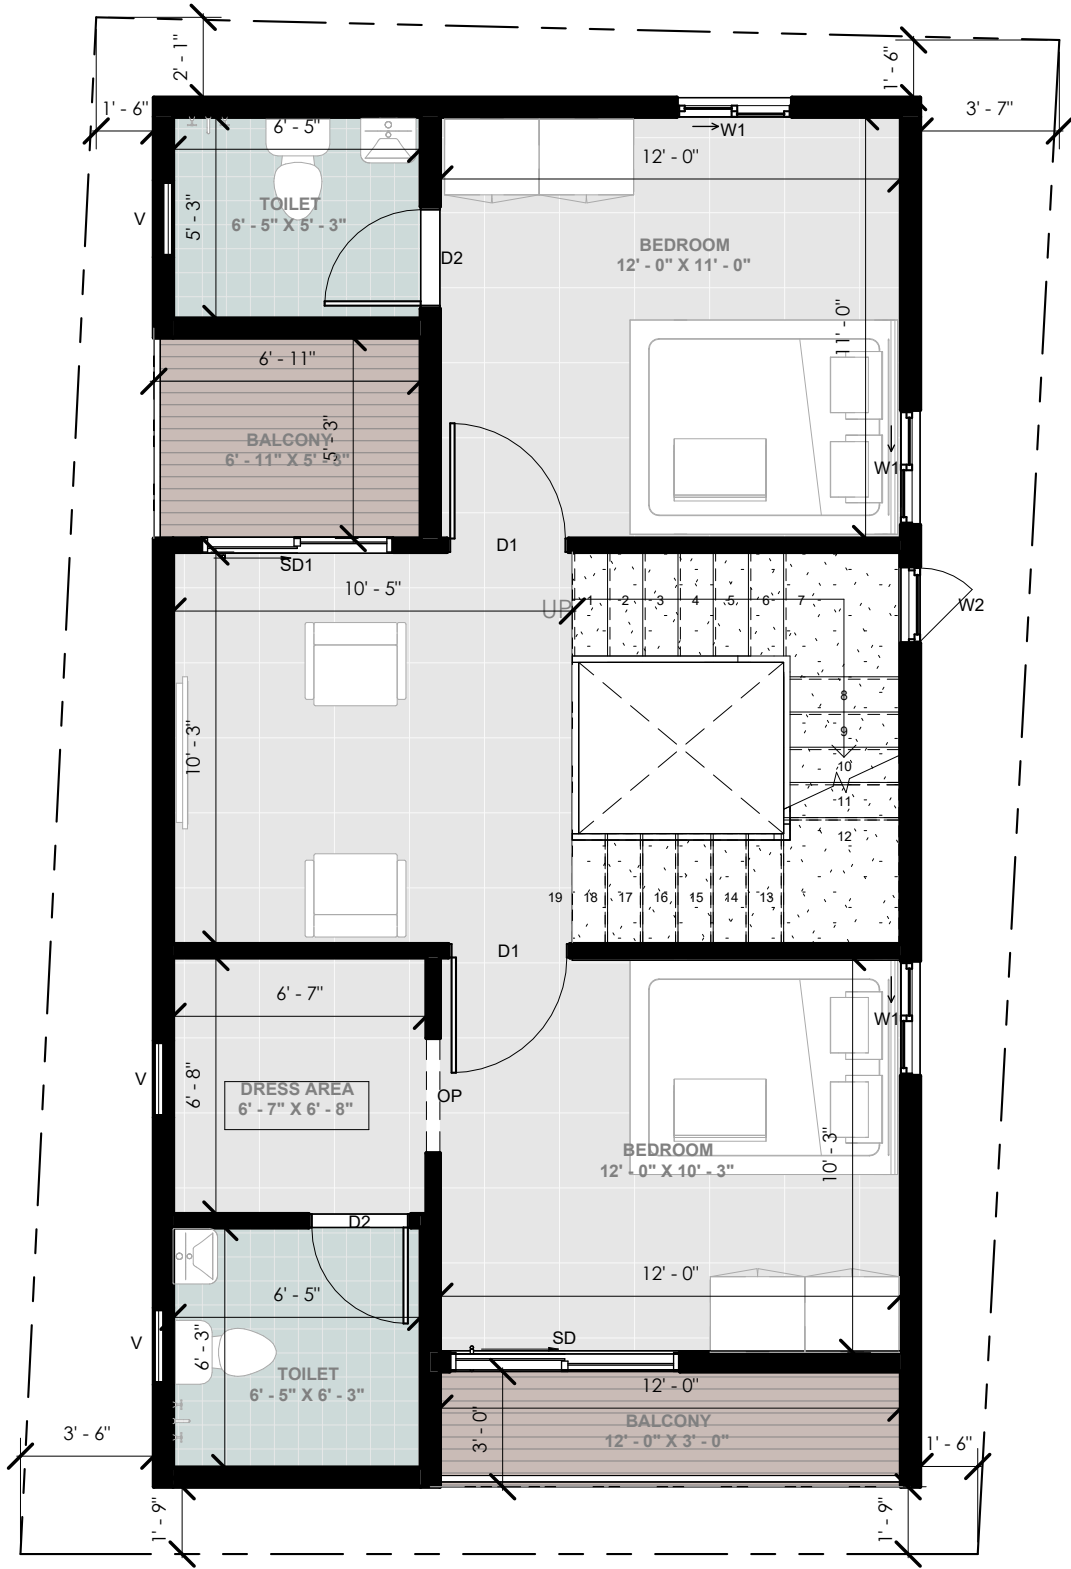

Door Schedule				
Mark	Width	Height	Count	Area

FIRST FLOOR LEVEL

D1	3' - 0"	7' - 0"	2	42 SF
D2	2' - 6"	7' - 0"	2	35 SF
OP	3' - 0"	7' - 0"	1	21 SF
SD	6' - 0"	8' - 0"	1	48 SF
SD1	5' - 0"	8' - 0"	1	40 SF

Window Schedule					
Mark	Sill Height	Width	Height	Count	Area

FIRST FLOOR LEVEL

V	6' - 0"	2' - 0"	2' - 0"	3	12 SF
W1	4' - 0"	3' - 0"	4' - 0"	3	36 SF
W2	5' - 0"	2' - 0"	2' - 0"	1	4 SF

NOTES:

- Opening schedule may change according to the structural design.
- The layout of columns and beams may change according to the structural design.
- Number of steps may change according to the plinth and parking height desired.
- Thickness of walls is only proposed. It may have to change based on the structural design to avoid column/beam projections.
- The contractor and the Consultant shall bear no responsibility whatsoever where any drawings provided by it/them in relation to the project / Said Works, does not comply with any applicable laws including the bye-laws of the building/society where such project is situated. Further, it is clarified that it shall be the responsibility of the Owner to ensure any and all compliance of the drawings provided by the Contractor/Consultant.
- Do not measure the drawing, Read all dimensions
- Contractor to check and verify all dimensions before commencing the work

REV.

CONCEPT - R1

AREA STATEMENT

Area Schedule (Gross Building)	
Name	Area
BUILTUP AREA	627 SF
PARKING	132 SF
FIRST FLOOR LEVEL	
BUILTUP AREA	649 SF



SUNKEN



LOFT

NOTES

EXTERNAL WALL-6" BLOCK WORK
INTERNAL WALL-4" BLOCK WORK
PLINTH HEIGHT -2'0" FROM ROAD LEVEL
PARKING HEIGHT-1'6" FROM ROAD LEVEL
NO OF STEPS-19 NO
RISER-6.3"
TREAD-10"
FFL-10'0"
HEADROOM NEEDED WITH 10'0"
TOILETS ARE SUNKEN
MAIN DOORS, SD1 SHOULD BE 8 FT HIEGHT

ARCHITECT

Ar. AKSHAYAA

Brick & Bolt

Brick&Bolt (PluckWalk Technologies Pvt. Ltd.) Urban Vault Koramangala 57, 60 Feet Rd, KHB Colony, 6th Block, Koramangala, Bengaluru,Karnataka 560095

Project
Residence for Mrs.
PARVATHI

CRN
CRN574114

Drg. No.
A102

Date
5-03-26

Drawing Title
FIRST FLOOR PLAN

Scale
1 : 60

