


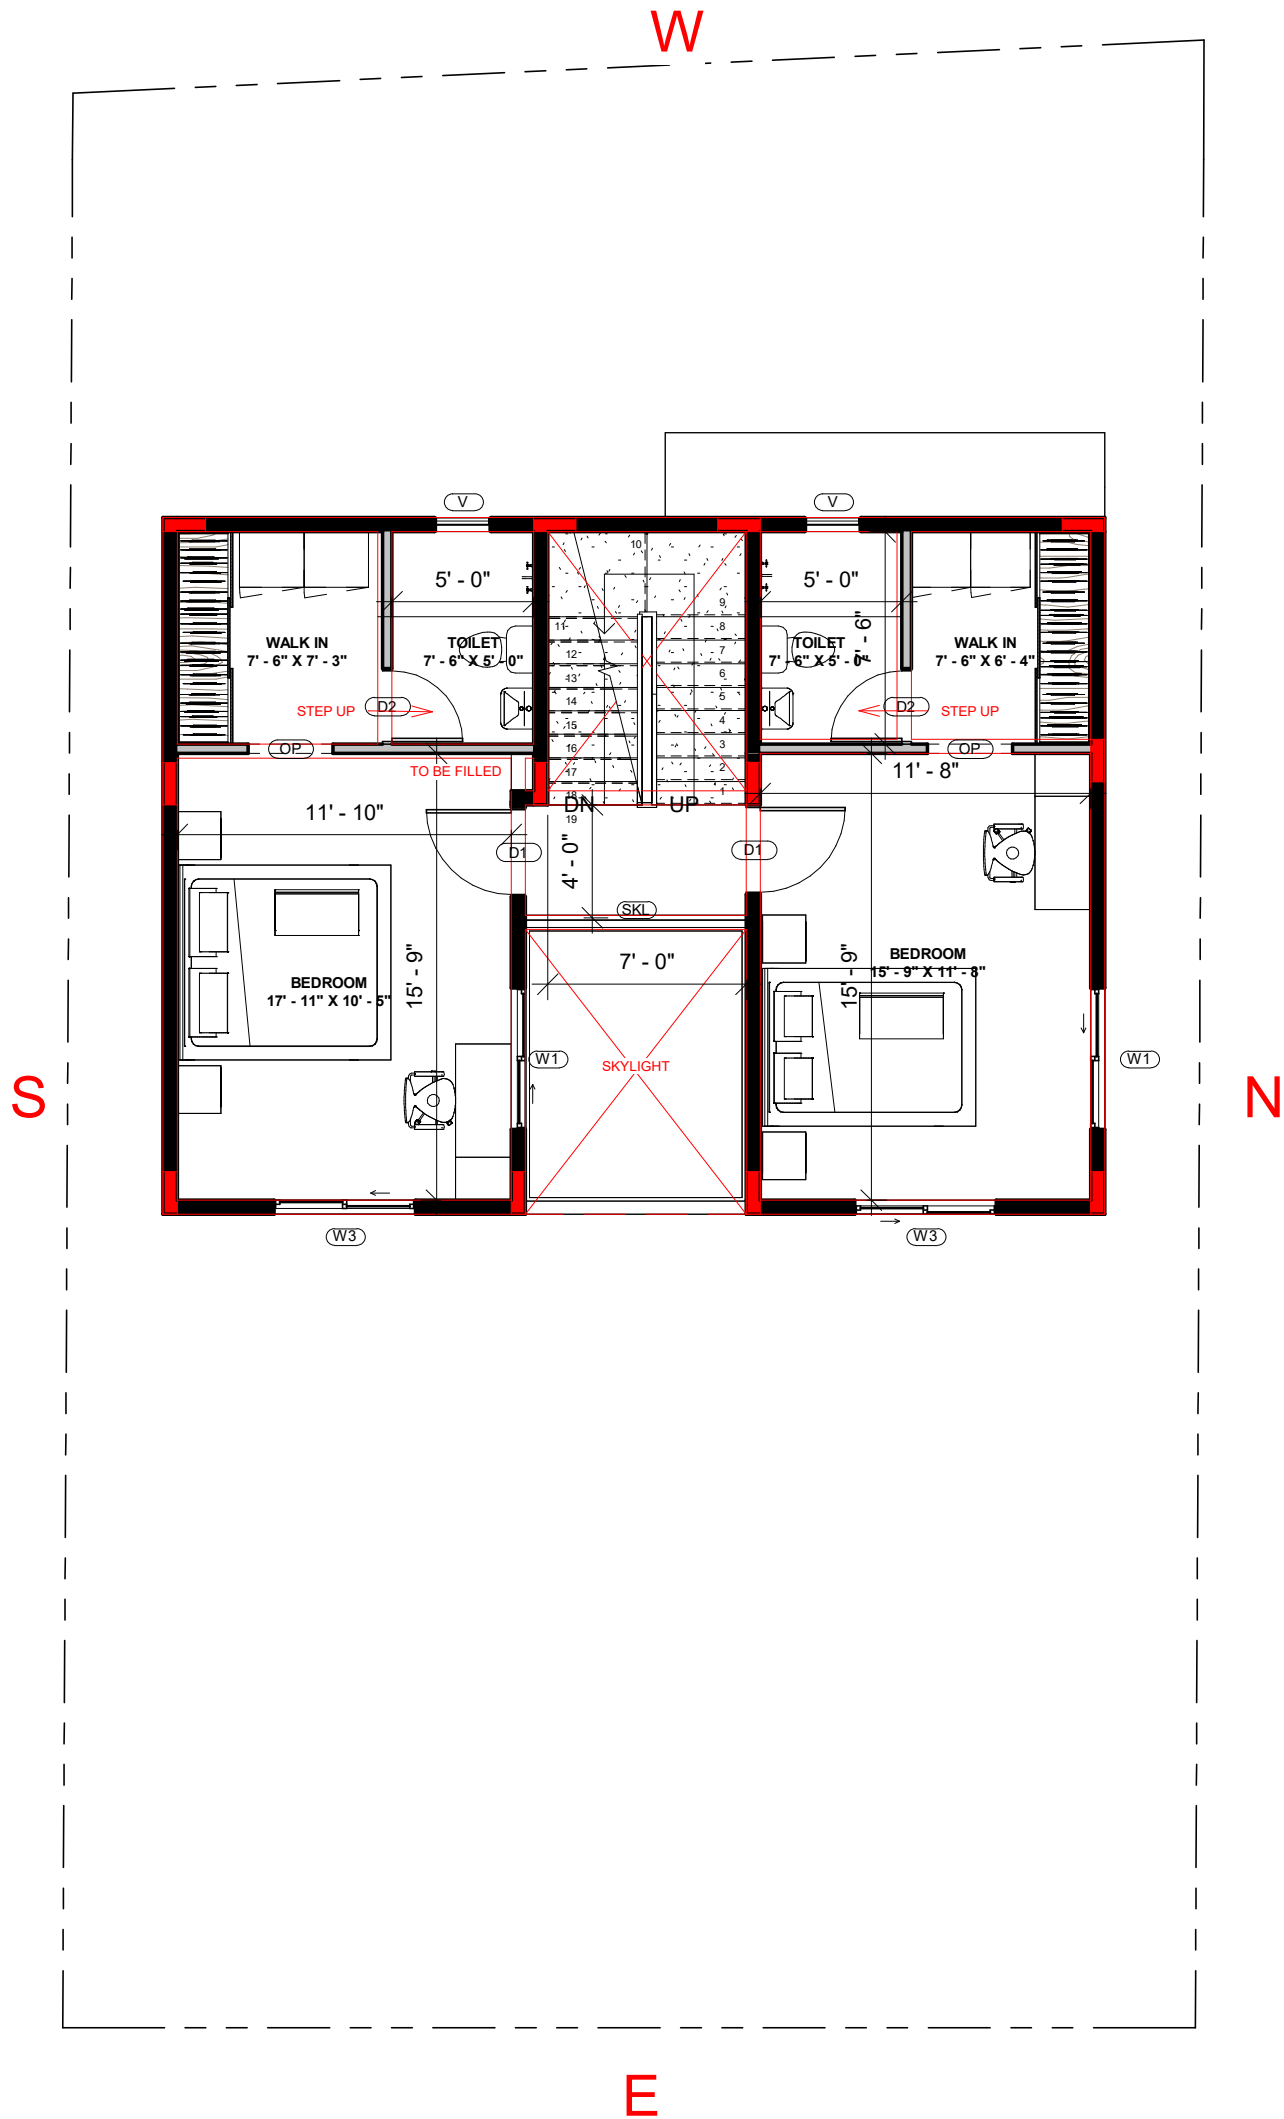

NOTES:

- Opening schedule may change according to the structural design.
- The layout of columns and beams may change according to the structural design.
- Number of steps may change according to the plinth and parking height desired.
- Wall thickness is proposed. It may have to change based on the structural design to avoid column/beam projections.
- All dimensions are in feet and inches
- Do not measure the drawing. Read all dimensions.
- Contractor to check and verify all dimensions before commencing the work
- The Contractor and the Consultant shall bear no responsibility whatsoever where any drawings provided by it/them in relation to the project/ Said works, does not comply with any applicable laws including the bye-laws of the building/ society where such project is situated. Further, it is clarified that it shall be the responsibility of the owner to ensure any and all compliance of the drawings provided by the Contractor /Consultant

REV.  
CONCEPT - R2

AREA STATEMENT

| Area Schedule (Gross Building) |               |
|--------------------------------|---------------|
|                                | Area          |
| <b>FIRST FLOOR LEVEL</b>       |               |
| <b>BUILTUP AREA</b>            | <b>744 SF</b> |

NOTES

EXTERNAL WALL-6" BLOCK WORK  
INTERNAL WALL-4" BLOCK WORK  
PARKING HEIGHT -1'0" FROM ROAD LVL  
PLINTH HEIGHT -2'0" FROM ROAD LVL  
NO OF STEPS -19 NOS  
RISER - 6.3"  
THREAD -10"  
STAIR WIDTH -3'2"  
FFL TO FFL -10'0"

ARCHITECT  
AR . VIDHUSHINI  
  
CHECKED BY  
AR. DHEERAJ