


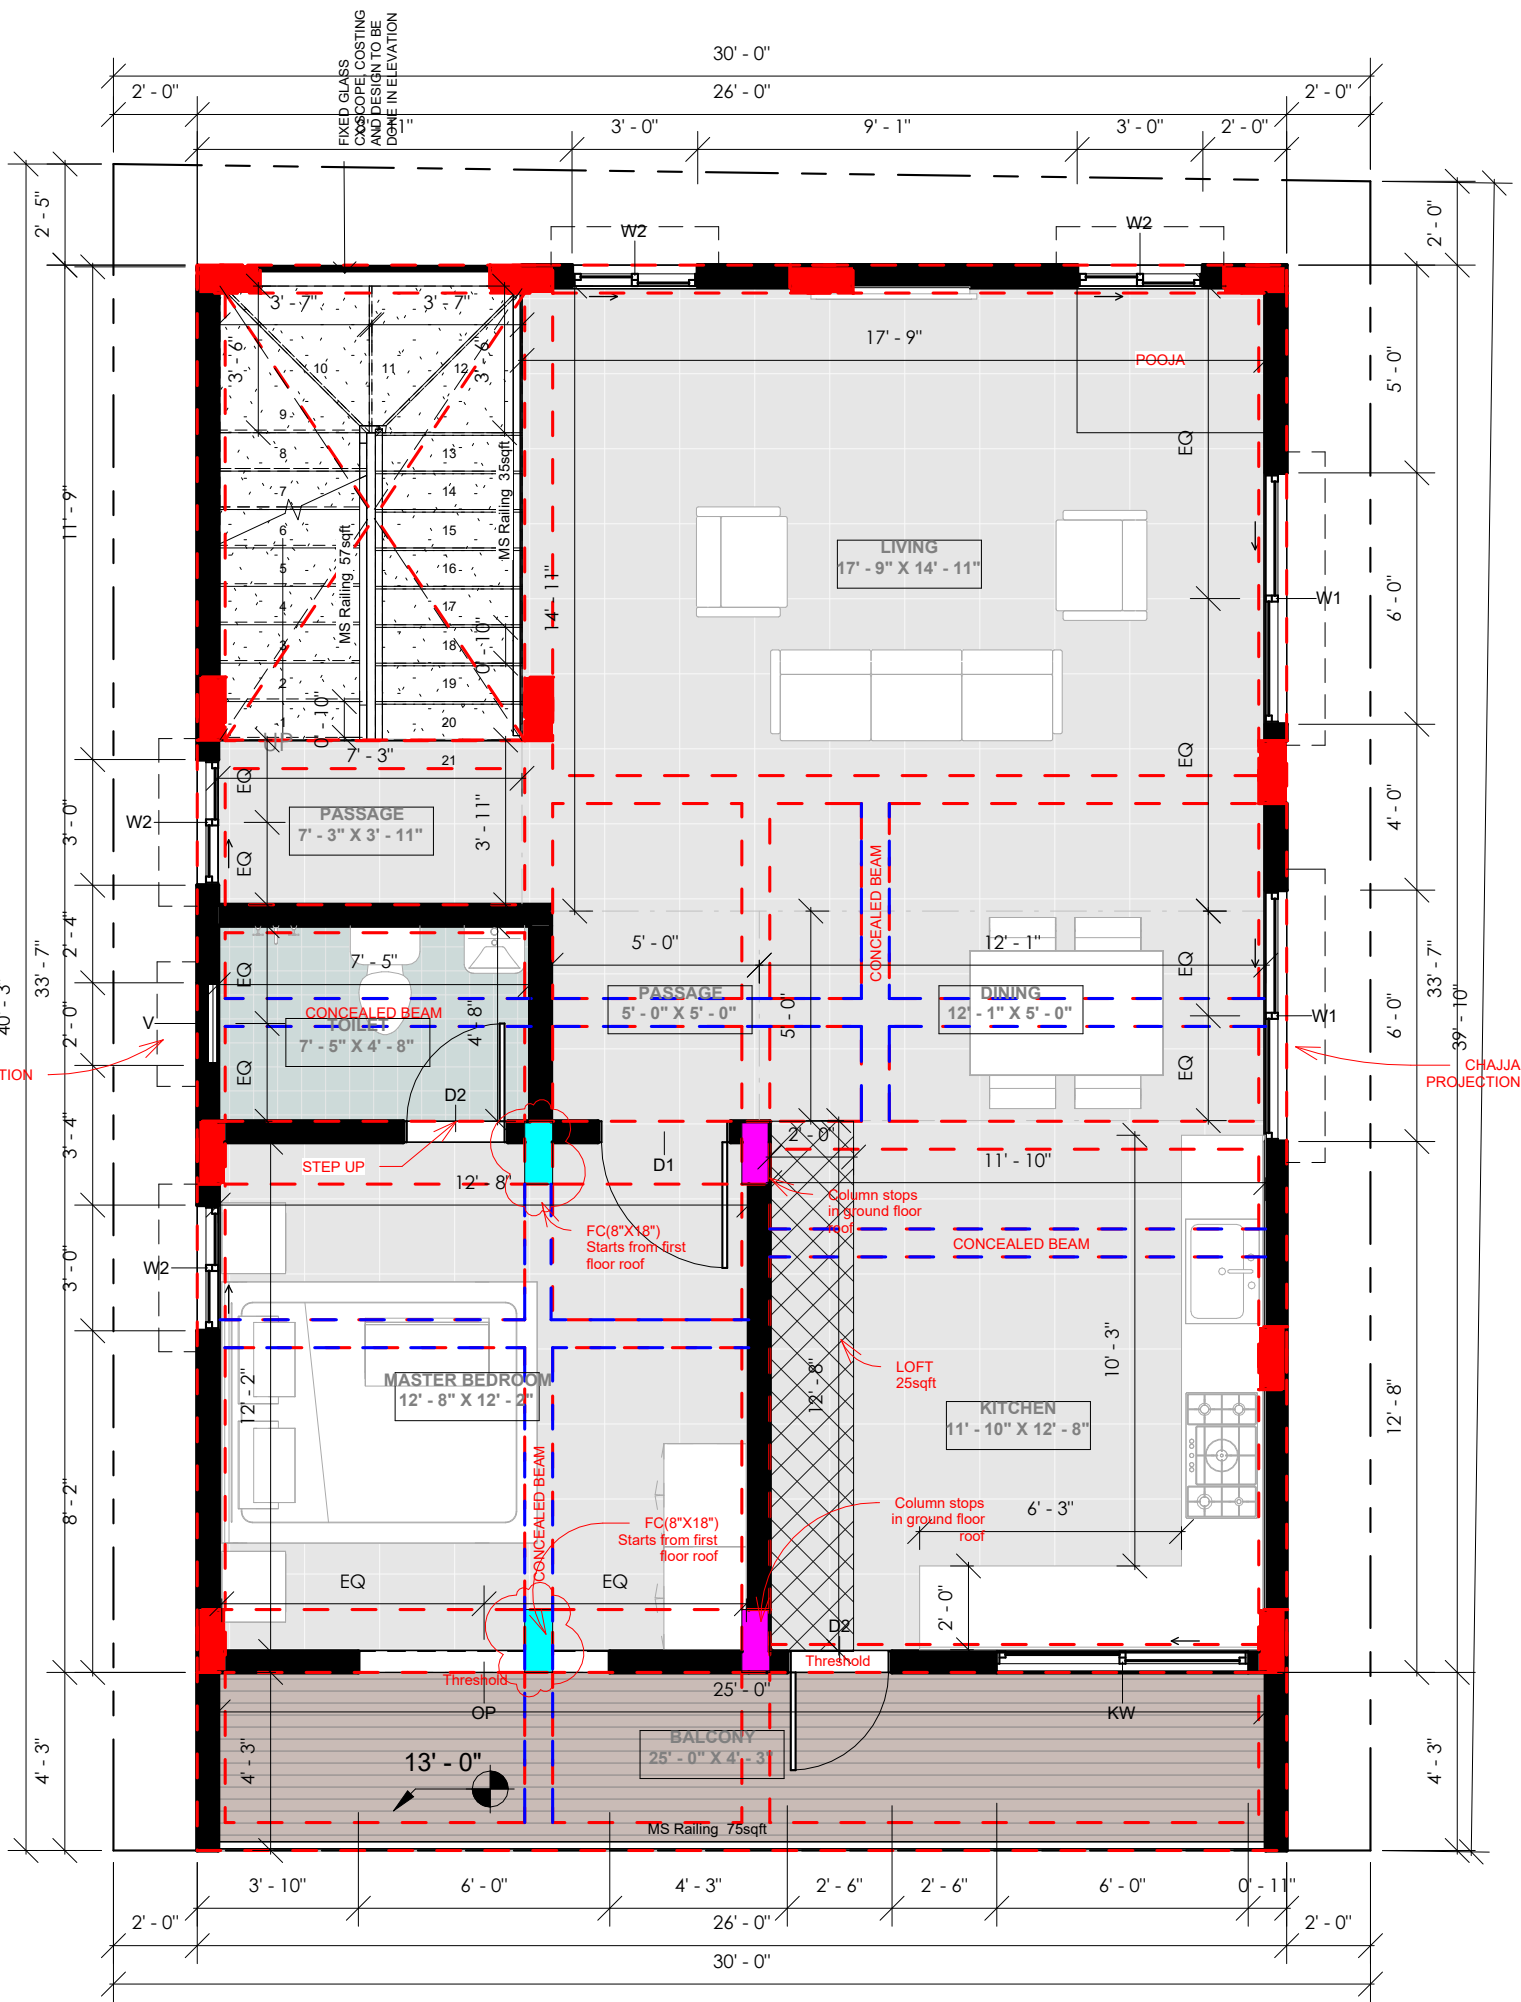

Door Schedule				
Mark	Width	Height	Count	Area

FIRST FLOOR LEVEL				
D1	3' - 0"	7' - 0"	1	21 SF
D2	2' - 4"	7' - 0"	2	33 SF
OP	6' - 0"	7' - 0"	1	42 SF

Window Schedule					
Mark	Sill Height	Width	Height	Count	Area

FIRST FLOOR LEVEL					
KW	4' - 0"	6' - 0"	3' - 0"	1	18 SF
V	5' - 0"	2' - 0"	2' - 0"	1	4 SF
W1	1' - 0"	6' - 0"	5' - 0"	2	60 SF
W2	2' - 0"	3' - 0"	5' - 0"	4	60 SF

- NOTES:**
- Opening schedule may change according to the structural design.
 - The layout of columns and beams may change according to the structural design.
 - Number of steps may change according to the plinth and parking height desired.
 - Thickness of walls is only proposed. It may have to change based on the structural design to avoid column/beam projections
 - The Contractor and the Consultant shall bear no responsibility whatsoever where any drawings provided by it/them in relation to the project / Said Works, does not comply with any applicable laws including the bye-laws of the building/society where such project is situated. Further, it is clarified that it shall be the responsibility of the Owner to ensure any and all compliance of the drawings provided by the Contractor/Consultant.
 - All dimensions are in ft and inches and All levels are in ft and inches.
 - Do not measure the drawing. Read all dimensions. All the notes in same size

REV.

Area Statement	
Area Schedule (Gross Building)	
Name	Area

FIRST FLOOR LEVEL	
BUILT UP AREA	877 SF
BALCONY	110 SF

- NOTES**
- MAIN GATE- ADDED IN THE QUOTE
COMPOUND WALL- ADDED IN THE QUOTE
MAIN DOORS AND INTERNAL DOORS
DESCOPED FROM THE PROJECT, CX SCOPE.
WINDOWS, WINDOW GRILL ARE ALSO
DESCOPED FROM THE PROJECT, CX SCOPE.
PLINTH HEIGHT IS ADDITIONAL ADDED IN
THE QUOTE.
- FLOOR HEIGHT
GROUND FLOOR -11'
FIRST FLOOR-11'
SECOND FLOOR -11'
TERRACE FLOOR-10'
STAIRCASE WIDTH-3'6"
NO OF STEPS-21
RISER HEIGHT:6.3"
THREAD-10"
SUMP PROPOSED:(9'X4'X6')-6000 liters
TOTAL WINDOW AREA: 427 Sqft
KINDLY REFER NGL IN DIGITAL SURVEY &
STRUCTURAL FULL SET DRAWING

6" EXTERNAL /INTERNAL WALL

DESIGNED BY:
Ar. AKSHAYAA

CHECKED BY
Ar. Dheeraj

